


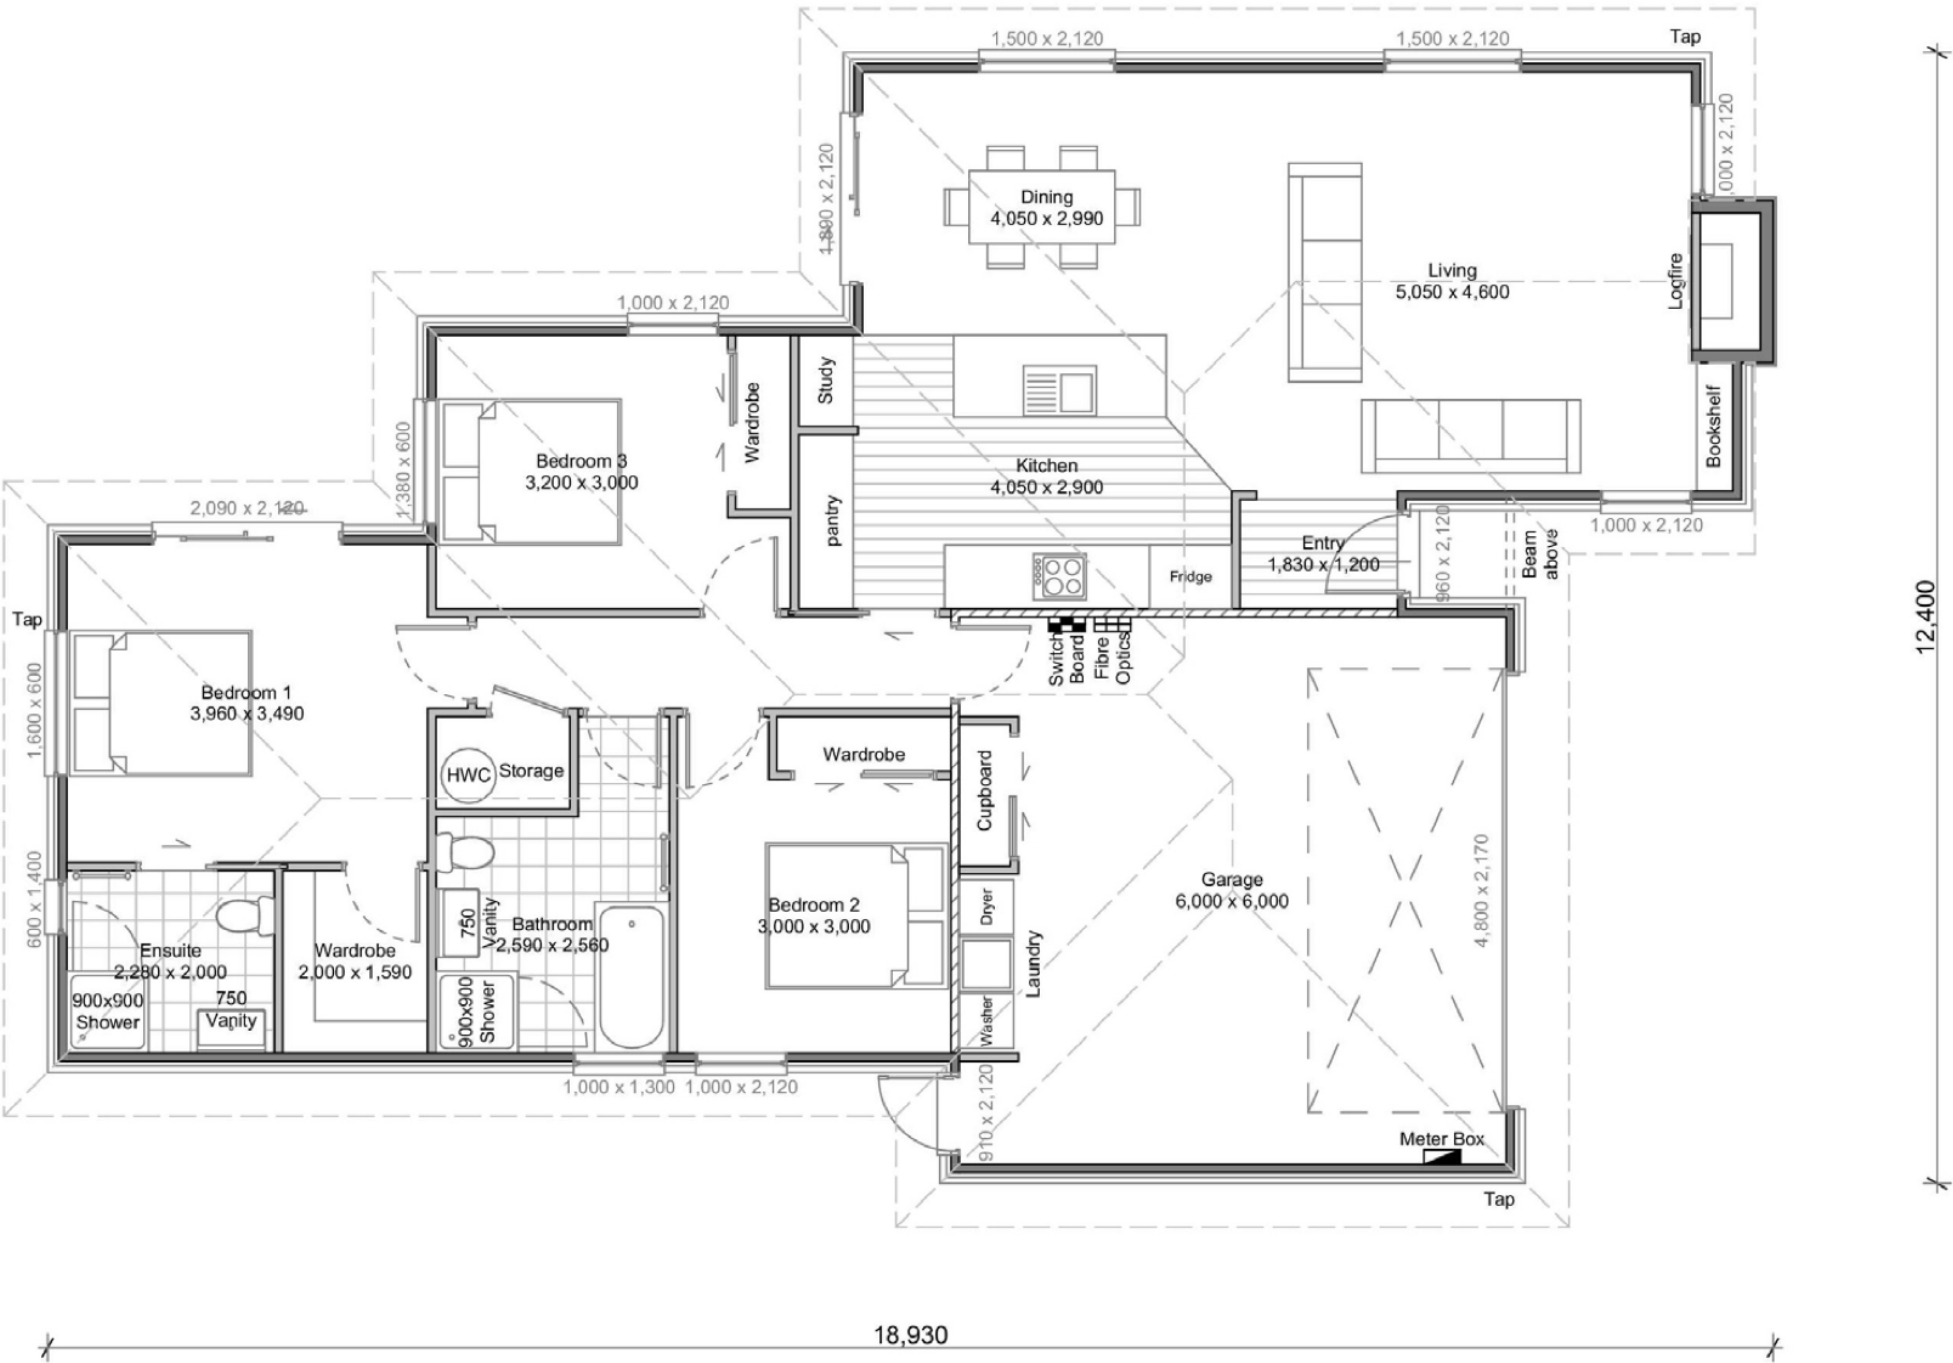

GROUND FLOOR PLAN

SCALE 1:100 @ A3

ALL DIMENSIONS IN MILLIMETRES

FOOTHILLS DESIGN STUDIO

Architectural Designers · LBP 117624
9 Mead Street, Rolleston 7614
design@foothills.co.nz
03 347 8821

CLIENT

B & K Whitcombe
Owner-occupier

PROJECT

New Dwelling
24 Tasman Crescent
Rolleston 7614
Lot 47 DP 581234
Selwyn District Council

REVISIONS

REV	DATE	DESCRIPTION	BY
A	10.03.26	Concept design	AM
B	01.04.26	Client review issue	AM
C	15.04.26	Building consent issue	AM
—			

PROJECT No. **2604**

DRAWN **AM** CHECKED **PR**

SCALE **1:100 @ A3** DATE **15.04.2026**

SHEET NAME
Ground Floor Plan

SHEET

A-101